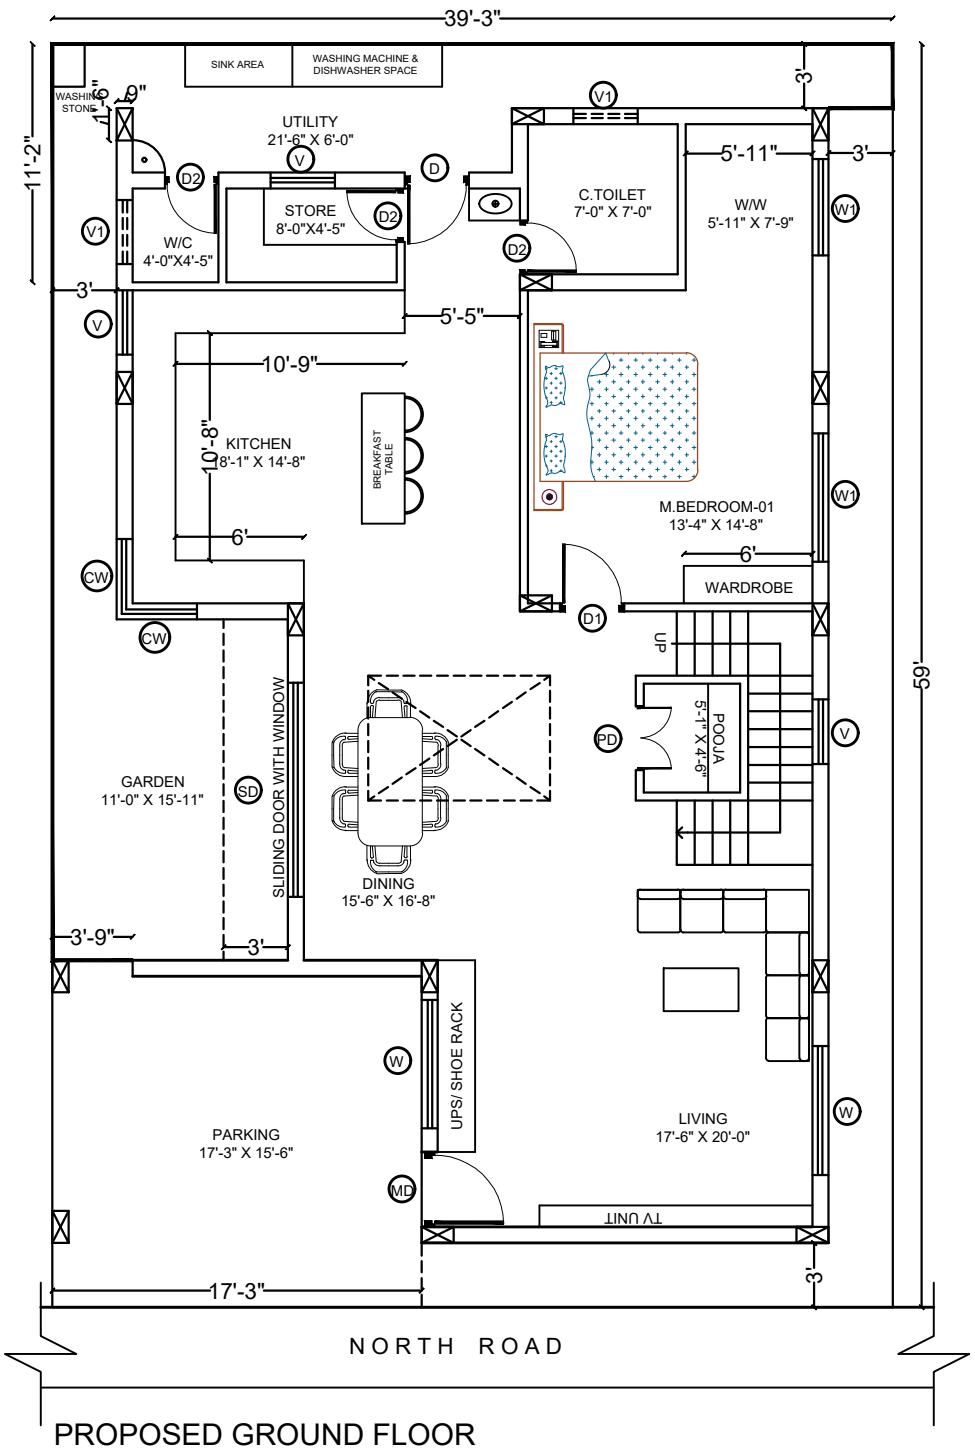


PROPOSED GROUND FLOOR

PROPOSED GROUND FLOOR PLAN

OPENING SCHEDULE

DOOR OPENING:

MD:3'-6" X 7'-0"X1no
PD:3'-0" X 7'-0"X1no
D:3'-0" X 7'-0"X1no
D1:3'-0" X 7'-0"X1no
D2:2'-6" X 7'-0"X3no
SD:10'-0" X 7'-0"X1no

WINDOW & VENTILATOR OPENING:
W : 6'-0" X 5'-0" X 2no
W1 : 4'-6" X 4'-0" X 2no
CW : 3'-6" X 3'-0" X 2no

V : 3'-0" X 3'-0" X 2no
V1 : 3'-0" X 2'-0" X 3no

ARCHIVING		
REV.No.	DATE	DESCRIPTION
R0	06-09-2023	PROPOSED GROUND FLOOR PLAN
R1	08-09-2023	PROPOSED GROUND FLOOR PLAN
R2	14-09-2023	PROPOSED GROUND FLOOR PLAN
R4		

SCHEME	CONCEPT	TENDER	GFC

CLIENT:
Mr.ASHWIN

PROJECT TITLE:

Proposed Residential Building
for Mr.Ashwin.

-

DESIGN TEAM	
DESIGN ENGG	PRABHU ANANDAN
CHECKED	
APPROVED	

SERVICE	SCHEMATIC LAYOUT		
TITLE	PROPOSED GROUND FLOOR PLAN		
DATE	14-02-2026	REV. R2	SCALE: NTS